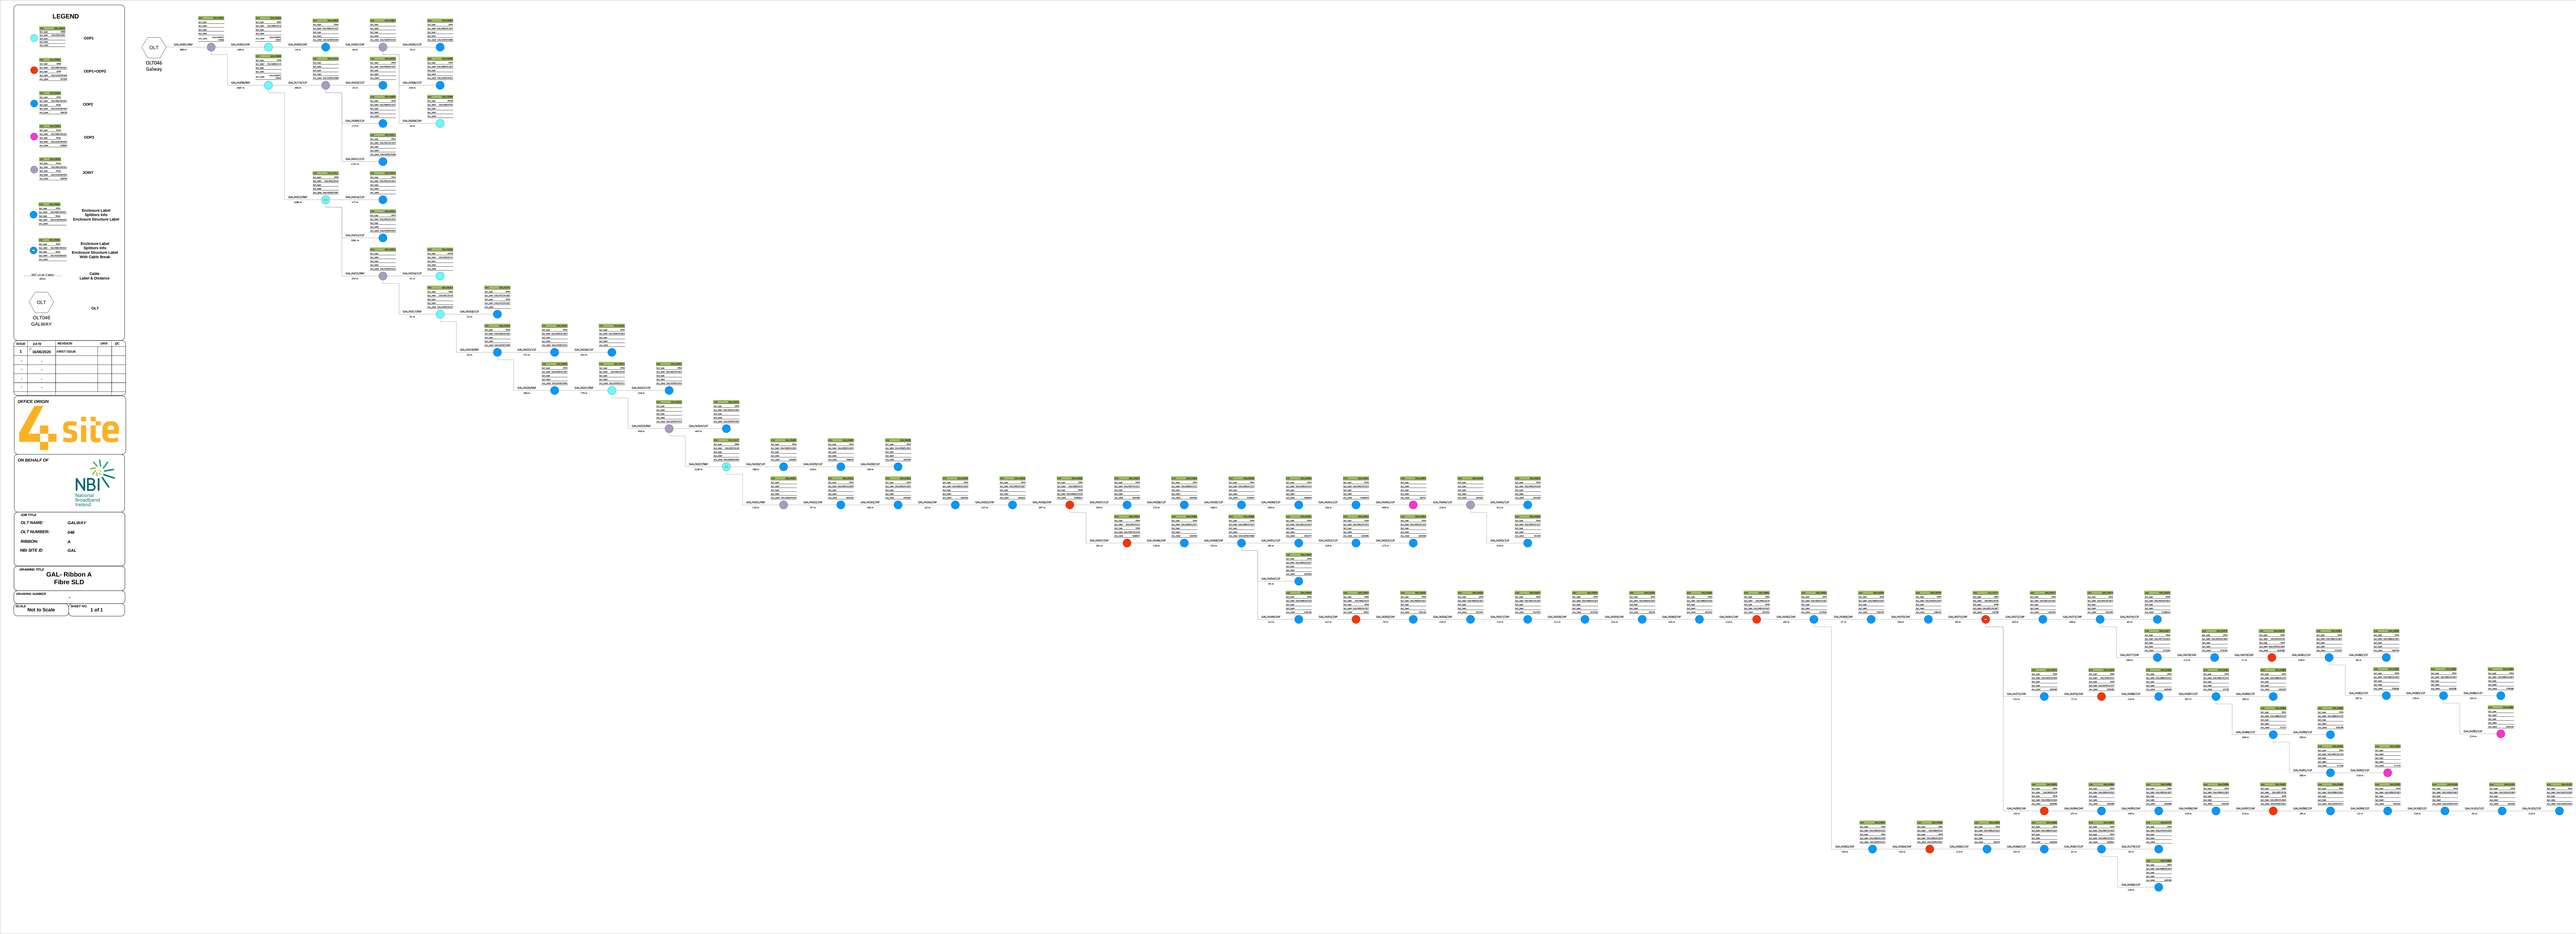
LEGEND
ODP1
ODP1+ODP2
ODP2
ODP3
JOINT
Enclosure Label
Splitters Info
Enclosure Structure Label
Enclosure Label
Splitters Info
Enclosure Structure Label
With Cable Break
Cable
Label & Distance
OLT
OLT046
GALWAY
ISSUE
DATE
REVISION
DRN
QC
1
10/06/2025
FIRST ISSUE
OFFICE ORIGIN
ON BEHALF OF
NBI
National Broadband Ireland
JOB TITLE
OLT NAME:
GALWAY
OLT NUMBER:
046
RIBBON:
A
NBI SITE ID
GAL
DRAWING TITLE
GAL- Ribbon A
Fibre SLD
DRAWING NUMBER
-
SCALE
Not to Scale
SHEET NO.
1 of 1
OLT
OLT046
Galway